TP104-D
TP104-C
TP104-B
TP104-A
5000
8500
3000
C/L BCU-106
5000
3500
550
550
1100
1100
1100
1100
1100
1100
800
1000
1000
250
750
450
125
TYP
125
TYP
TP104-1
TP104-2
TP104-3
3000
7000
3300
3700
C/L BCU-104A
TP4BM112
UB203X133X25
TP4BM111
UB203X133X25
ISMC150
ISMC100
ISMC100
ISMC150
TP4BM110
UB203X133X25
TP4BM119
ISMC100
TP4BM203
UB203X133X25
TP4PB116
ISA75X75X6
TP4PB118
ISA75X75X6
TP4BM149
UB533X210X101
TP4BM181
UB203X133X25
TP4BM204
ISMC150
TP4BM196
UB203X133X25
TP4BM107
ISMC150
TP4PB108
ISA75X75X6
TP4PB110
ISA75X75X6
TP4PB113
ISA75X75X6
TP4PB114
ISA75X75X6
TP4BM156
UB203X133X25
TP4PB120
ISA75X75X6
TP4PB130
ISA75X75X6
TP4BM167
ISMC100
TP4PB119
ISA75X75X6
TP4BM122
ISMC100
TP4BM178
ISMC100
TP4BM106
ISMC150
P20
400
360
500
600
500
200
600
800
1200
TP4BM121
ISMC100
TP4BM131
ISMC100
TP4BM143
ISMC100
TP4BM152
UB203X133X25
TP4BM161
ISMC100
TP4BM170
ISMC100
TP4PB129
ISA75X75X6
TP4PB121
ISA75X75X6
TP4BM188
UB203X133X25
TP4BM218
UB203X133X25
TP4PB104
ISA75X75X6
TP4BM120
UB254X146X37
TP4BM132
UB203X133X25
700
600
TP4BM169
ISMC100
TP4BM104
UB203X133X25
TP4BM109
UB203X133X25
TP4BM154
UB305X165X46
P15
TP4BM178
ISMC100
TP4BM202
UB203X133X25
TP4PB106
ISA90X90X8
TP4BM117
UB254X146X37
TP4BM129
UB254X146X37
TP4BM139
UB533X210X101
TP4BM145
UB254X146X37
1000
TP4BM160
UB254X146X37
TP4PB121
ISA75X75X6
TP4BM176
UB203X133X25
TP4PB128
ISA75X75X6
TP4BM187
UB203X133X25
400
1000
TP4BM124
UB254X146X37
TP4BM171
UB203X133X25
TP4BM195
UB203X133X25
TP4PB105
ISA90X90X8
TP4BM116
UB203X133X25
TP4BM128
UB203X133X25
TP4BM140
ISMC100
2000
= =
TP4BM163
ISMC100
TP4BM166
NPB400X180X66.3
TP4BM175
UB203X133X25
TP4PB127
ISA90X90X8
P17
580
250
TP4BM193
UB203X133X25
TP4BM201
UB203X133X25
200
1100
TP4BM122
ISMC100
TP4BM153
UB254X146X37
TP4BM168
ISMC100
TP4BM177
ISMC100
TP4BM183
ISMC100
TP4BM189
ISMC100
TP4BM209
ISMC100
1100
700
ISMC100
TP4PB107
ISA90X90X8
TP4BM227
PL20X250
PG-2
TP4BM130
ISMC100
TP4BM151
ISMC100
TP4BM230
ISMC100
P16
TP4PB125
ISA75X75X6
TP4BM232
ISMC100
TP4PB132
ISA75X75X6
TP4PB104
ISA75X75X6
TP4PB136
ISA90X90X8
TP4BM208
ISMC100
910
P11
P12
P13
P14
C
C
TP4PB103
ISA75X75X6
TP4BM115
UB254X146X37
TP4BM127
UB203X133X25
TP4BM138
UB203X133X25
TP4BM127
UB203X133X25
TP4BM127
UB203X133X25
TP4BM127
UB203X133X25
TP4BM127
UB203X133X25
TP4BM174
UB203X133X25
TP4PB123
ISA90X90X8
TP4BM186
UB203X133X25
TP4BM186
UB203X133X25
TP4BM199
UB305X165X46
TP4BM214
NPB450X190X77.57
1290
1500
TP4BM225
PL20X250
AT CD.+12.300M
PG-5
P26A
TP4BM123
ISMC100
3000
= BRG CRS =
TP4BM122
ISMC100
TP4BM155
ISMC100
4900
2700
TP4BM159
ISMC100
TP4BM167
ISMC100
TP4BM177
ISMC100
TP4BM182
ISMC100
TP4BM167
ISMC100
TP4BM206
ISMC100
2580
TP4PB102
ISA75X75X6
TP4BM122
ISMC100
TP4BM172
ISMC100
TP4PB122
ISA75X75X6
TP4BM197
ISMC100
1500
3503
2000
700
1000
1700
1500
1097
338
260
2700
1290
TP4BM147
UB610X229X125
P14
P18
270
580
TP4BM198
UB305X165X46
B
B
TP4PB101
ISA90X90X8
TP4BM114
UB203X133X25
TP4BM126
UB203X133X25
4095
TP4BM137
UB203X133X25
P25
TP4BM150
UB203X133X25
TP4BM158
UB203X133X25
TP4BM162
UB203X133X25
TP4BM165
UB203X133X25
TP4BM173
UB203X133X25
TP4PB126
ISA75X75X6
3900
TP4BM228
PL20X250
PG-2
TP4BM185
UB203X133X25
TP4BM200
UB203X133X25
TP4BM205
ISMC150
1550
ISMC100
ISMC150
ISMC100
1200
1410
TP4BM122
ISMC100
TP4BM142
ISMC100
TP4BM231
ISMC100
TP4BM122
ISMC100
TP4BM177
ISMC100
TP4BM184
ISMC100
TP4BM207
ISMC150
A
A
TP4BM113
UB203X133X25
TP4BM118
ISMC150
570
TP4PB111
ISA75X75X6
TP4PB115
ISA75X75X6
TP4PB117
ISA75X75X6
TP4PB111
ISA75X75X6
TP4PB124
ISA75X75X6
TP4PB133
ISA75X75X6
TP4PB134
ISA75X75X6
TP4BM210
ISMC150
360
390
1000
1000
TP4BM148
NPB450X190X77.57
TP4BM190
UB254X146X37
TP4BM193
UB203X133X25
ISMC100
ISMC100
ISMC150
TP4PB137
ISA75X75X6
355
TP4BM146
ISMC100
360
120
1450
750
1100
795
305
1103
1097
1100
800
1000
1000
520
480

PLAN AT CD. +13.150M

SCALE 1:40

ALL PLAN BRACE ARE 100M BELOW (TOS)

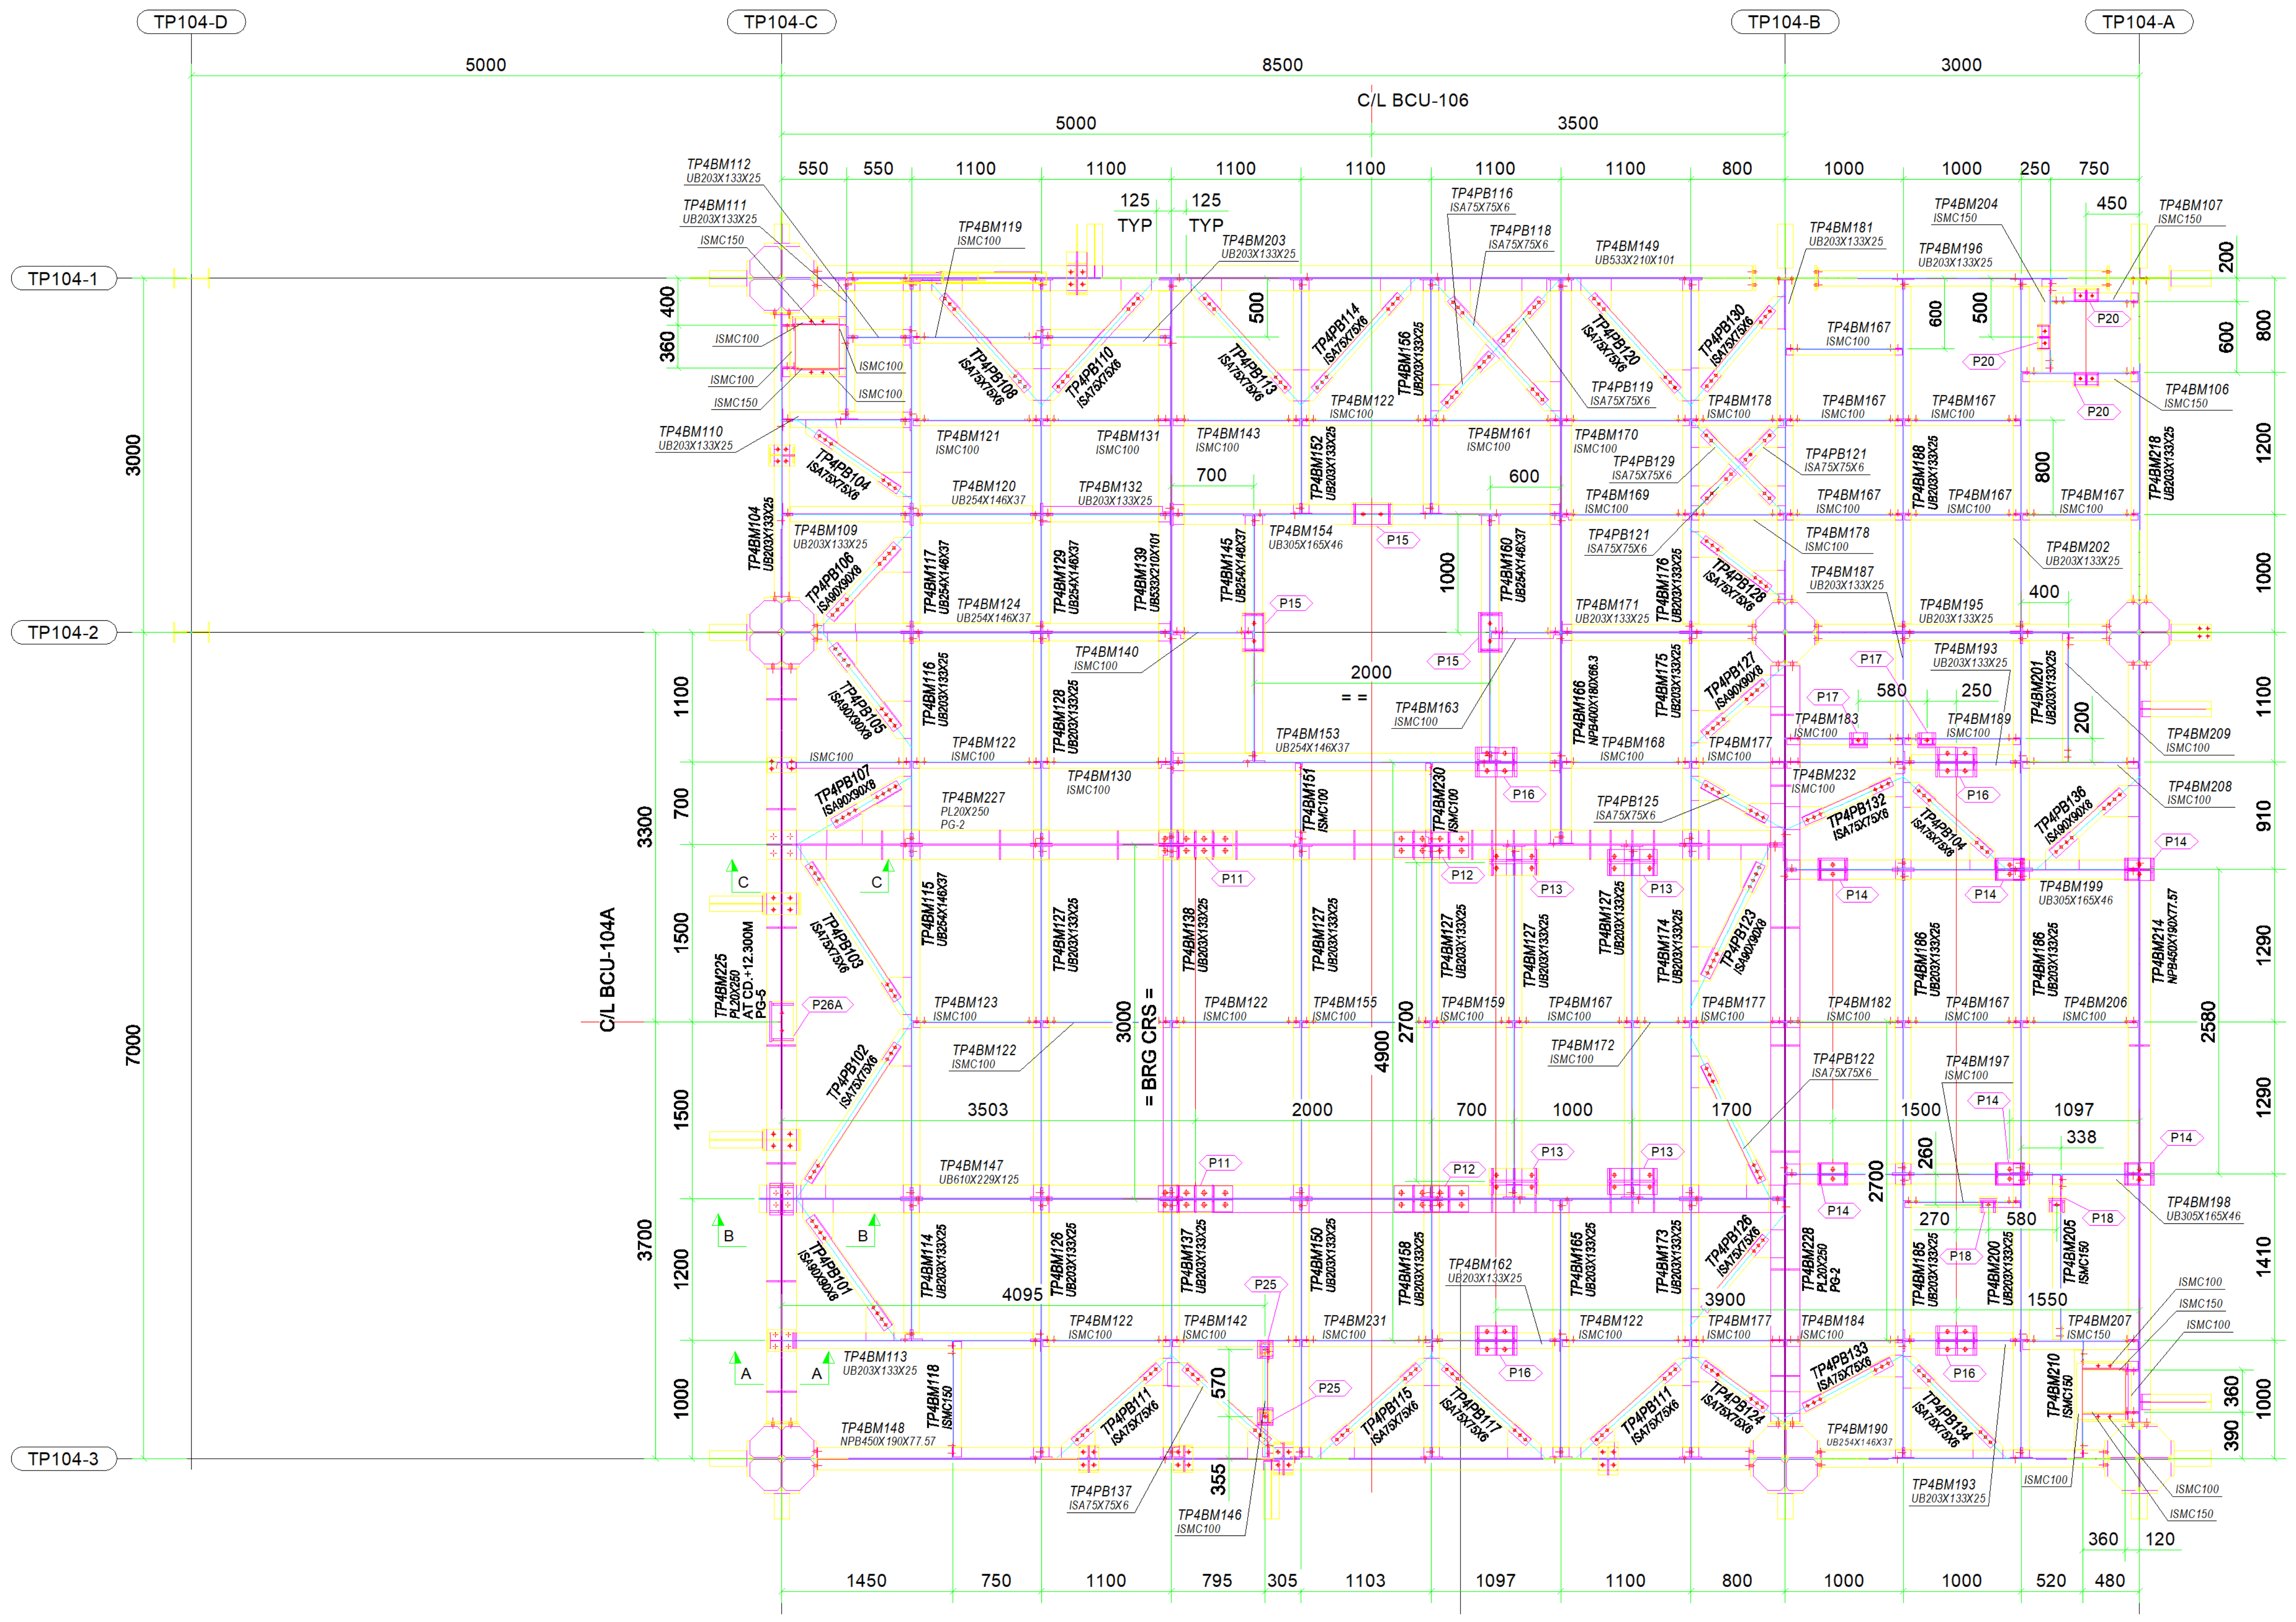
TP104-D
TP104-C
TP104-B
TP104-A
TP104-1
TP104-2
TP104-3
5000
8500
3000
C/L BCU-106
5000
3500
550
550
1100
1100
1100
1100
1100
1100
800
1000
1000
250
750
125
125
TYP
TYP
3000
7000
1100
700
1500
1500
1200
1000
3300
3700
C/L BCU-104A
= BRG CRS =
1450
750
1100
795
305
1103
1097
1100
800
1000
1000
520
480
360
120
800
1200
1000
1100
910
1290
1290
1410
1000
2580
P11
P12
P13
P14
P15
P16
P17
P18
P20
P25
P26A

PLAN AT CD. +13.150M

SCALE 1:40

ALL PLAN BRACE ARE 100M BELOW (TOS)