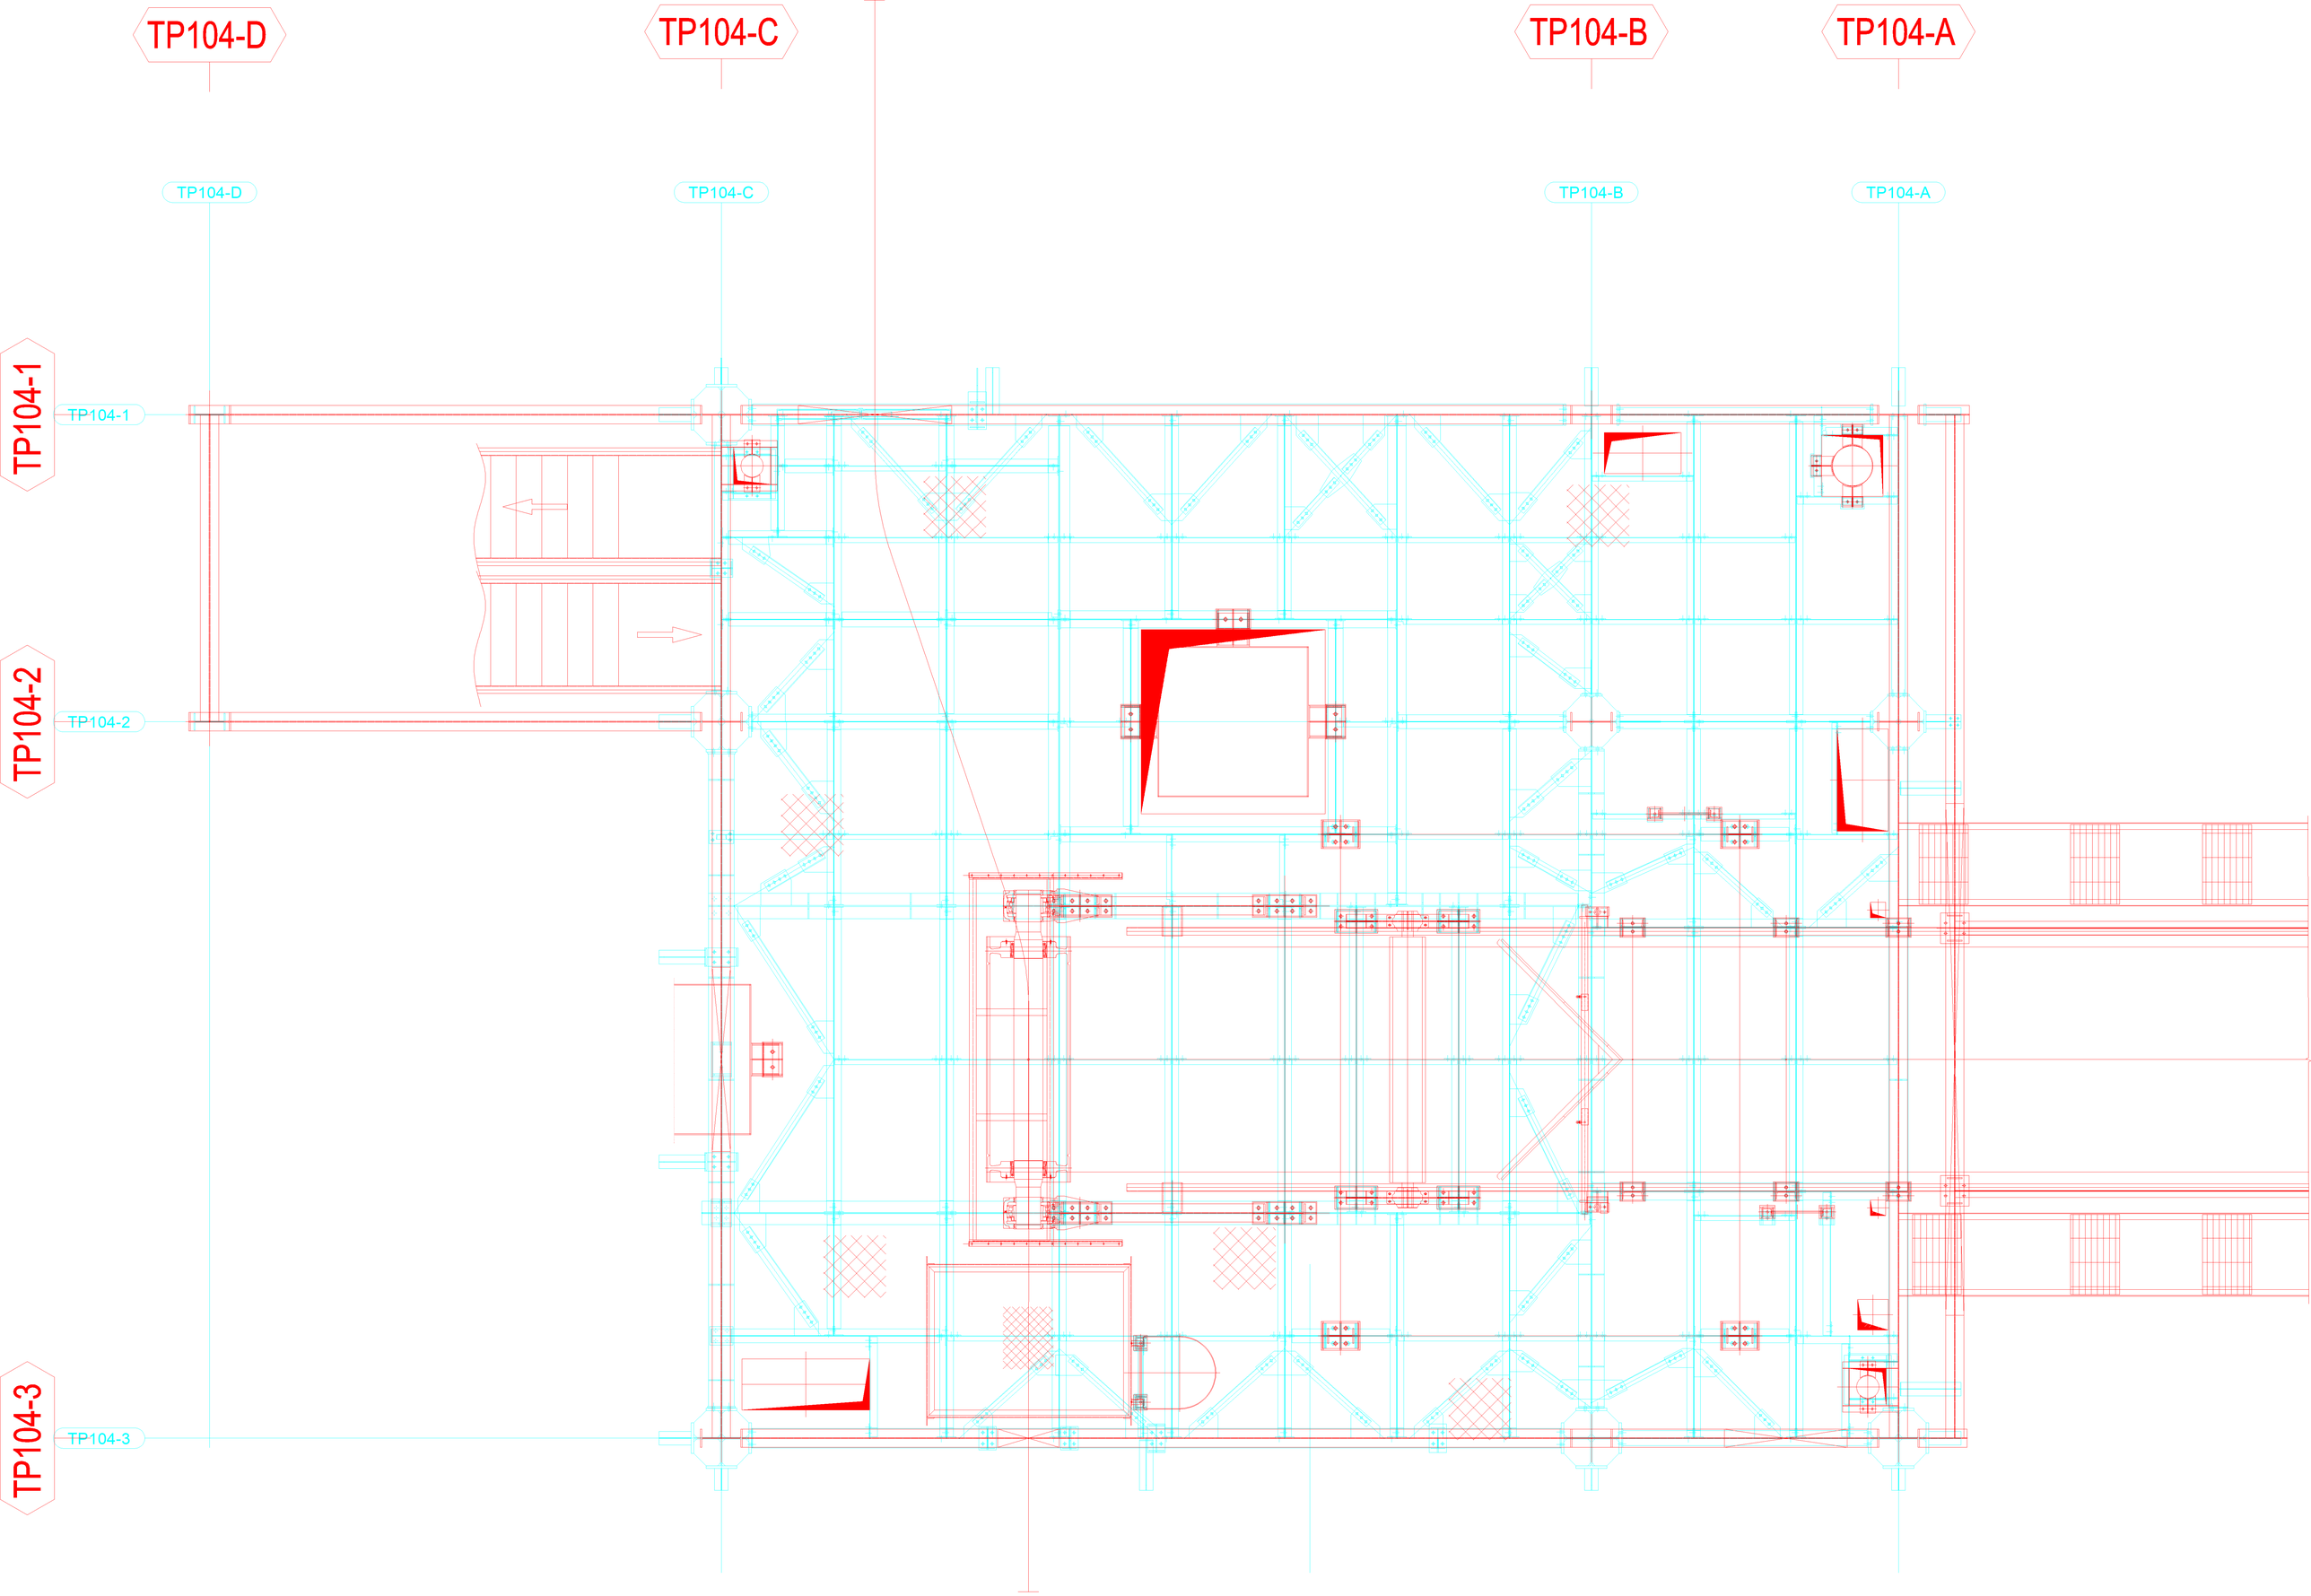



PLAN AT CD. +13.150M

SCALE 1:40

ALL PLAN BRACE ARE 100M BELOW (TOS)

FLOOR PLAN AT LVL CD(+)13.150M (T.O.S)

(SCALE-1:75)

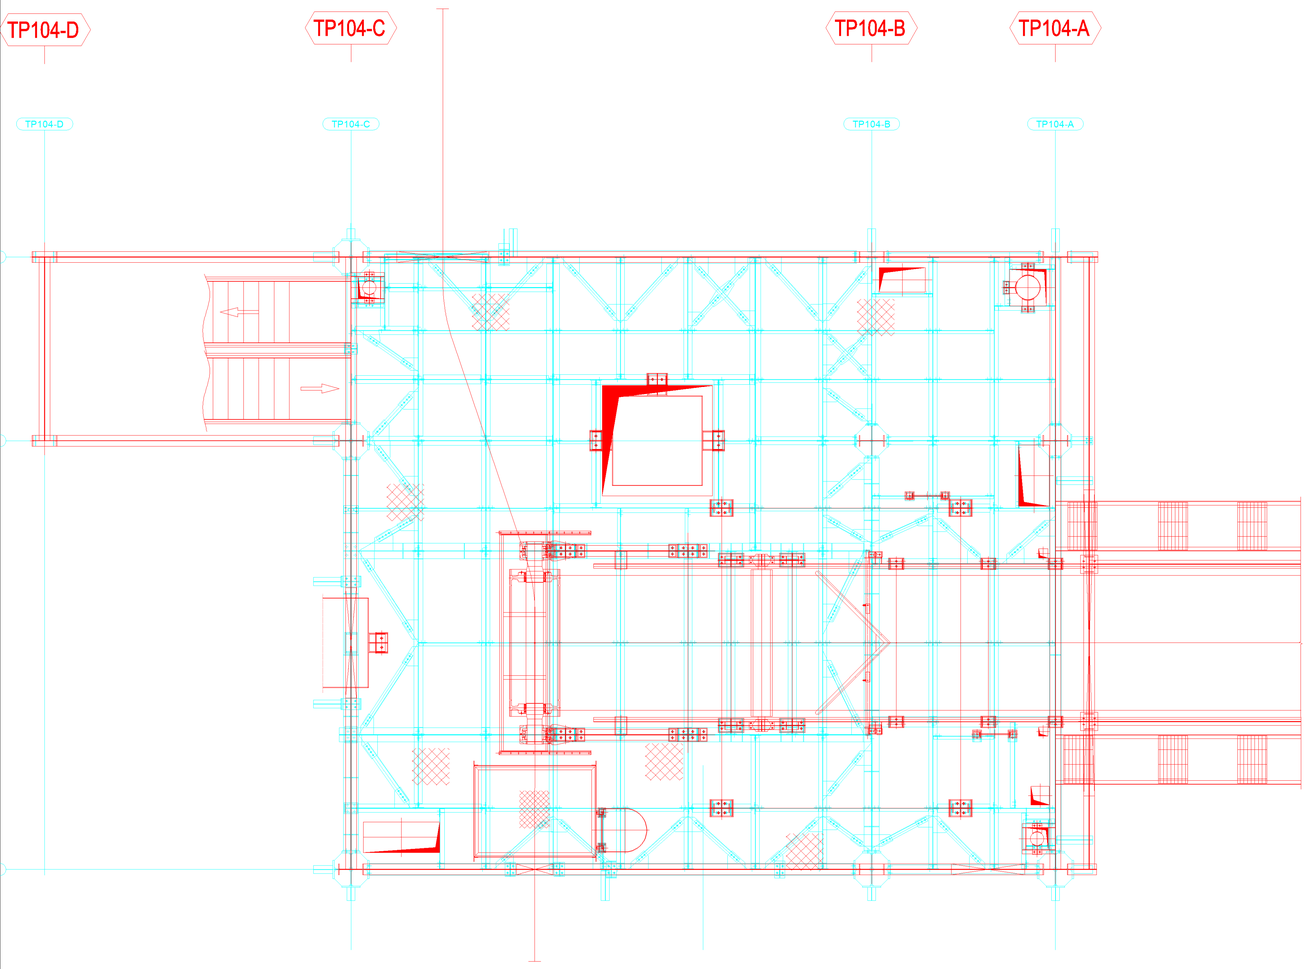

PLAN AT CD. +13.150M

SCALE 1:40

ALL PLAN BRACE ARE 100M BELOW (TOS)

FLOOR PLAN AT LVL CD(+)13.150M (T.O.S)

(SCALE-1:75)